

مجتمع مسکونی-تجاری

زمین ۵۴۲/۳۸ m² - اصفهان

عنوان نقشه

پلان همکف / پیلوت

تراز

±۰.۰۰ متر

مقیاس

۱:۱۵۰

شماره برگه

A-۱۰۱

تاریخ

۱۴۰۵/۰۶/۲۷

زیربنا

۲۱۱.۳ m²

جدول فضاها

مغازه ۱

۴۴.۹۰

۵.۹۹×۷.۵۰

مغازه ۲

۴۴.۹۰

۵.۹۹×۷.۵۰

مغازه ۳

۴۴.۹۰

۵.۹۹×۷.۵۰

انبار/سرویس

۵۷.۵

پارکینگ

۶ فضا

۲.۵۰×۵.۰۰

لابی و هسته

۲۱.۴

۴.۲۰×۵.۱۰

ارتفاع مفید پیلوت ۲.۴۰ m معاف از تراکم

مغازه ۵.۴۰ m با نیم طبقه در تراز +۲.۶۰


ارتفاع

واقعی پارکینگ ۱۲ تا ۱۴ فضا؛ اینجا ۶ فضا

نیاز

یا جریمه تبصره ۵ ماده ۱۰۰ جبران شود

کسری با زیرزمین

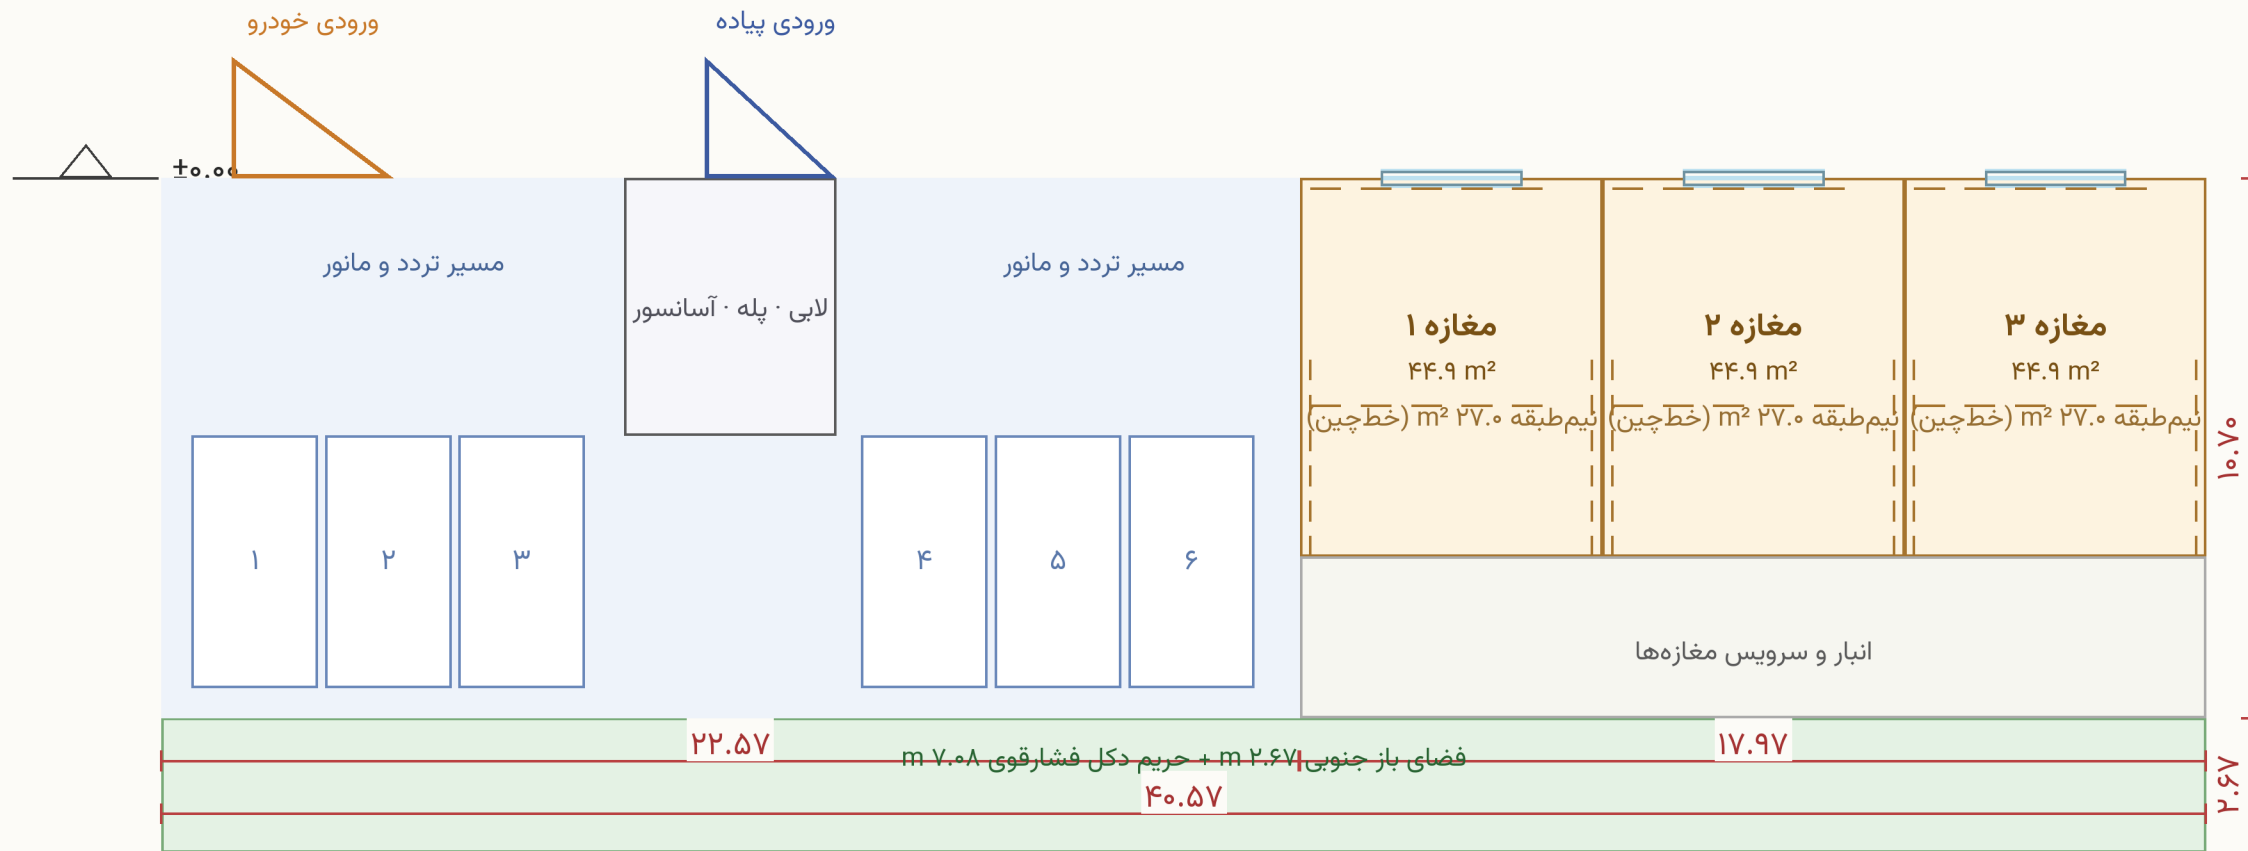

۵ متر

مقیاس ۱:۱۵۰