# مجتمع مسکونی-تجاری

زمین ۵۴۲٫۳۸ m² — اصفهان

عنوان نقشه
**پلان طبقه تیپ**

تراز
**+۵.۴۰ متر**

مقیاس
**۱:۱۰۰**

شماره برگه
**A-۱۰۳**

تاریخ
**۱۴۰۵/۰۶/۲۷**

زیربنا
**۱۹۰.۵ m²**

## جدول فضاها


| | | |
|---|---|---|
| نشیمن | ۲۵.۱۲ | ۶.۵۶×۳.۸۳ |
| آشپزخانه | ۱۰.۰۶ | ۲.۶۳×۳.۸۳ |
| سرویس | ۲.۴۲ | ۱.۳۹×۱.۷۴ |
| حمام | ۴.۵۲ | ۲.۶۰×۱.۷۴ |
| هال / ورودی | ۹.۰۴ | ۵.۲۰×۱.۷۴ |
| خواب ۱ | ۱۴.۰۳ | ۵.۱۴×۲.۷۳ |
| خواب ۲ | ۱۱.۰۵ | ۴.۰۵×۲.۷۳ |
| ایوان | ۱۵.۷۰ | ۶.۵۶×۲.۴۰ |
| پله/آسانسور/پاگرد | ۲۲.۳۰ | — |
| شفت نور و تهویه | ۱۲.۶ | ۴.۲۰×۳.۰۰ |

· هسته و همسایگی ۲۵cm · تیغه ۱۵cm دیوار پیرامونی ۳۰cm

· پله رفت‌وبرگشتی ۱۶ پله (۲۹cm×۱۸.۱m) ارتفاع طبقه ۲.۹۰

باز می‌شود (جایگزین: ادغام = ۶.۹ m²) سرویس از داخل حمام

واحد ۹۲.۰ m² = ۷۶.۲ m² بسته + ۱۵.۷ ایوان هر

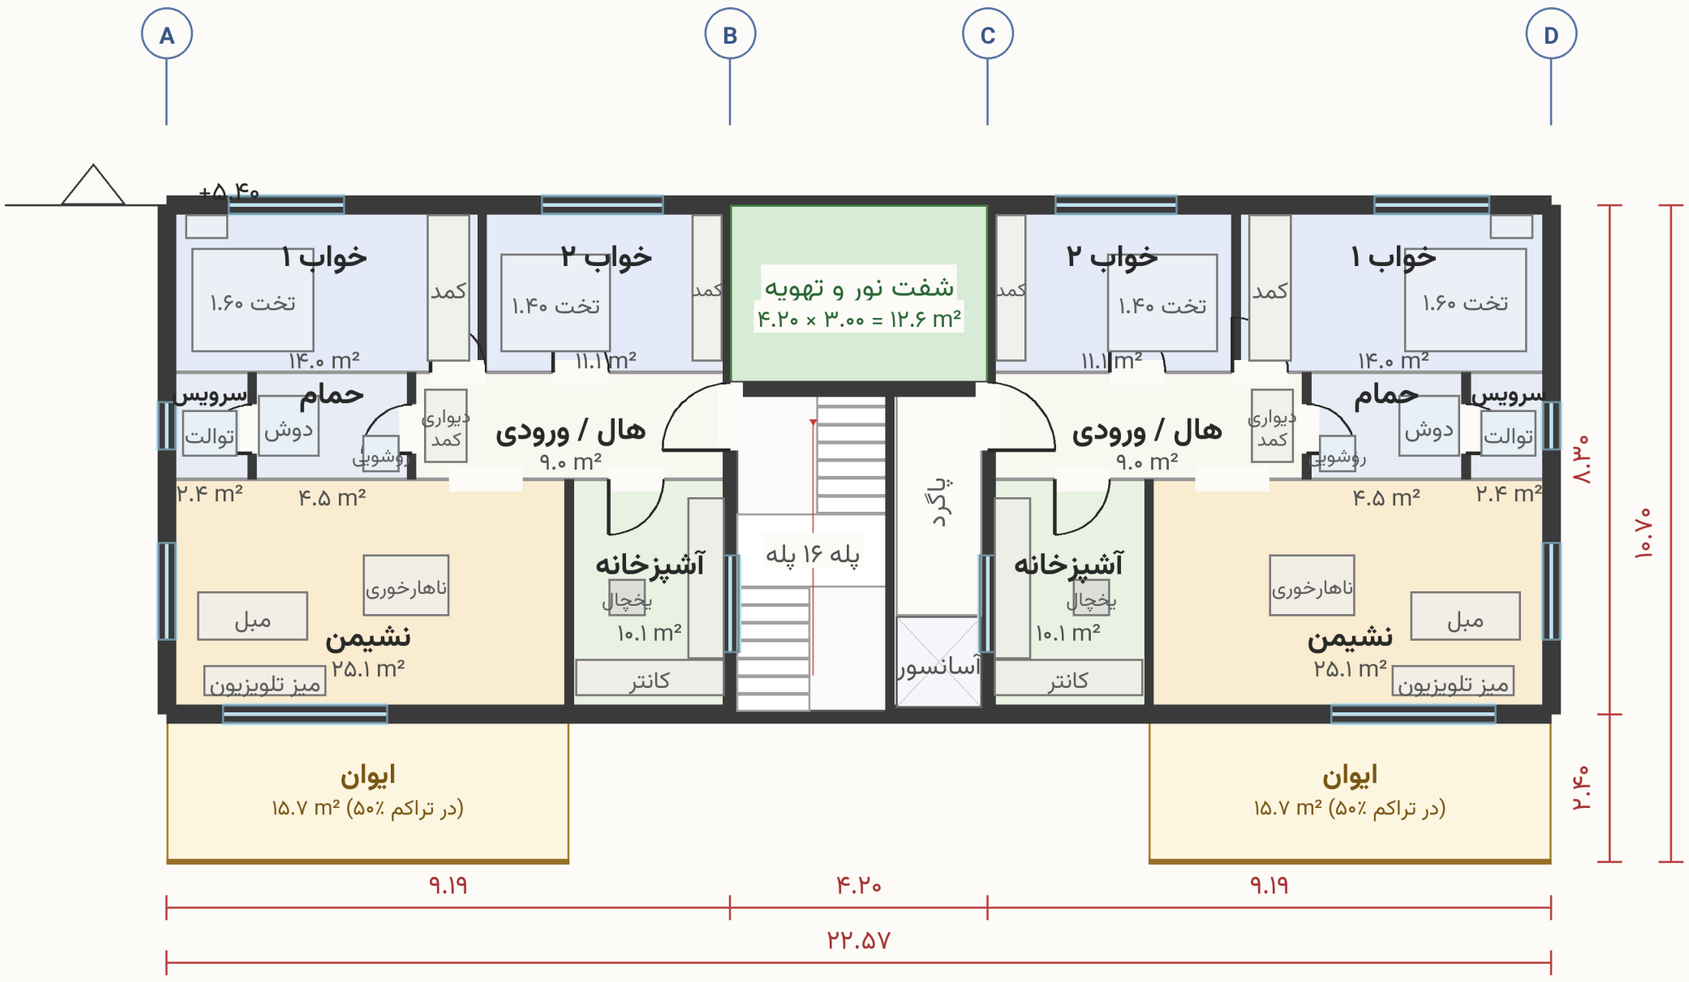


شمال

۰ ۵ متر

مقیاس ۱:۱۰۰