

مجتمع مسکونی-تجاری

زمین ۵۴۲/۳۸ m² - اصفهان

عنوان نقشه

پلان همکف / پیلوت

تراز

±۰.۰۰ متر

مقیاس

۱:۱۵۰

شماره برگه

A-۱۰۱

تاریخ

۱۴۰۵/۰۶/۲۷


زیربنا

۲۱۱.۳ m²

جدول فضاها

مغازه ۱	۴۴.۹۰
۵.۹۹×۷.۵۰	
مغازه ۲	۴۴.۹۰
۵.۹۹×۷.۵۰	
مغازه ۳	۴۴.۹۰
۵.۹۹×۷.۵۰	
انبار/سرویس	۵۷.۵
-	
پارکینگ	۶ فضا
۲.۵۰×۵.۰۰	
لابی و هسته	۲۱.۴
۴.۲۰×۵.۱۰	

ارتفاع مفید پیلوت ۲.۴۰ m معاف از تراکم
مغازه ۵.۴۰ m با نیم طبقه در تراز +۲.۶۰
ارتفاع
واقعی پارکینگ ۱۲ تا ۱۴ فضا؛ اینجا ۶ فضا
نیاز
یا جریمه تبصره ۵ ماده ۱۰۰ جبران شود
کسری با زیرزمین

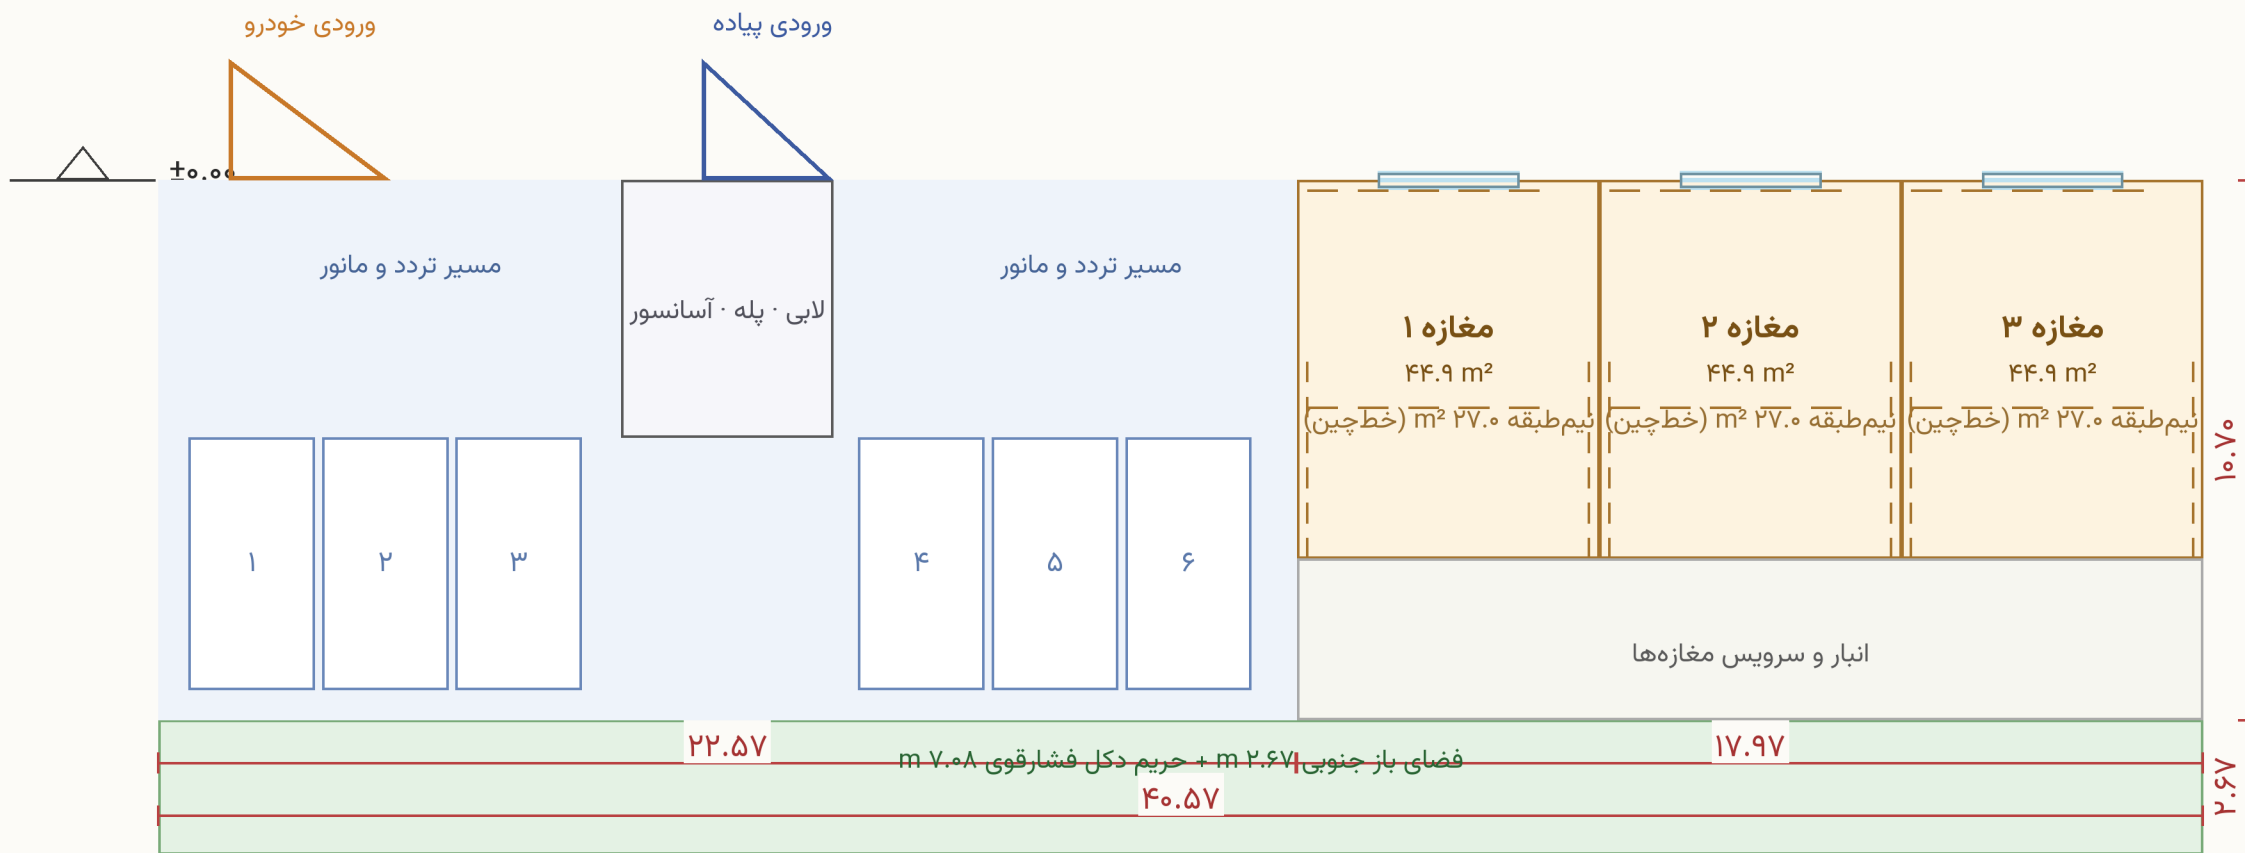

شمال

۵ متر

مقیاس ۱:۱۵۰

مجتمع مسکونی-تجاری

زمین ۵۴۲/۳۸ m² - اصفهان

عنوان نقشه

نیم طبقه و انباری

تراز

۲.۶۰+ متر

مقیاس

1:150

شماره برگه

A-102

تاریخ

1405/06/27

زیربنا

انباری ۴۰ m²

جدول فضاها

۴۰.۰ انباری (۸ واحد)
هرکدام ۵.۰ m²


۲۷.۰ نیم طبقه ۱
۵.۹۹×۴.۵۰

۲۷.۰ نیم طبقه ۲
۵.۹۹×۴.۵۰

۲۷.۰ نیم طبقه ۳
۵.۹۹×۴.۵۰

نیم طبقه تا ۵۵٪ مساحت مغازه مجاز است
تنها ۲۰٪ آن (۱۶.۲ m² از ۸۰.۹ m²) در تراکم
با ارتفاع مفید ۲.۲۰ m کاملاً معاف از تراکم
انباری

ارتفاع مفید نیم طبقه ۲.۵۰ m

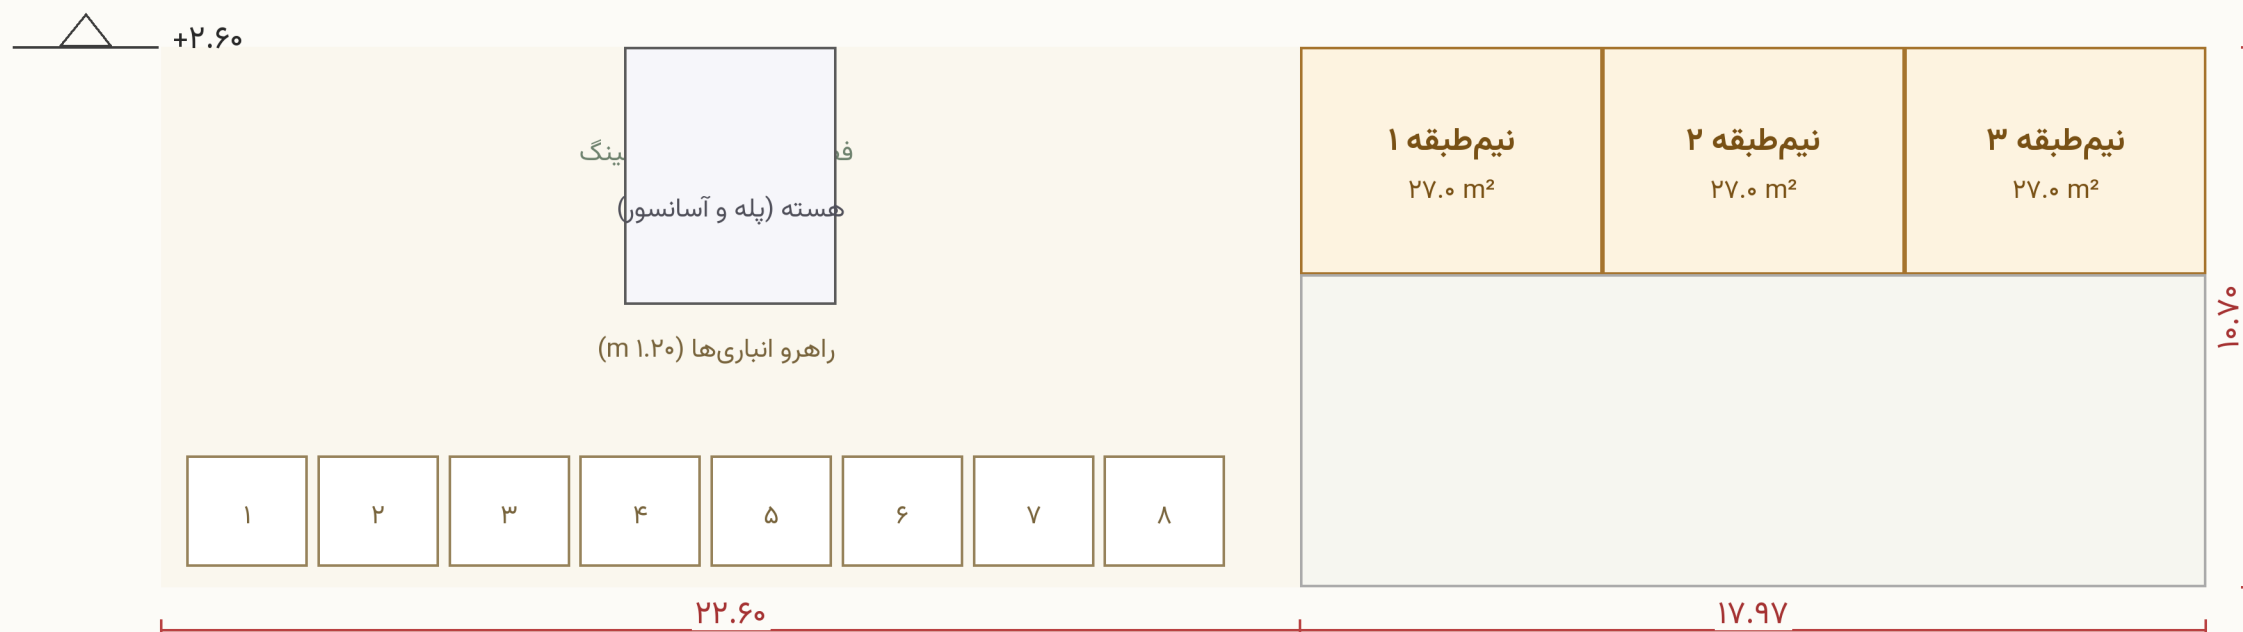

٥ متر

مقياس ١:١٥٠

مجتمع مسکونی-تجاری

زمین ۵۴۲/۳۸ m² – اصفهان

عنوان نقشه

پلان طبقه تپ

تراز

۵.۴۰+ متر

مقیاس

۱:۱۰۰

شماره برگه

A-۱۰۳

تاریخ

۱۴۰۵/۰۶/۲۷

زیربنا

۱۹۰.۵ m²

جدول فضاها

نشیمین ۲۵.۱۲

۶.۵۶×۳.۸۳

آشپزخانه ۱۰.۰۶

۲.۶۳×۳.۸۳

سرویس ۲.۴۲

۱.۳۹×۱.۷۴

حمام ۴.۵۲

۲.۶۰×۱.۷۴

هال / ورودی ۹.۰۴

۵.۲۰×۱.۷۴

خواب ۱ ۱۴.۰۳

۵.۱۴×۲.۷۳

خواب ۲ ۱۱.۰۵

۴.۰۵×۲.۷۳

ایوان ۱۵.۷۰

۶.۵۶×۲.۴۰

پله/آسانسور/پاگرد ۲۲.۳۰

–

شفت نور و تهویه ۱۲.۶

۴.۲۰×۳.۰۰

· هسته و همسایگی ۲۵cm · تیغه ۱۵cm

دیوار پیرامونی ۳۰cm

· m · پله رفت و برگشتی ۱۶ پله (۱۸.۱×۲۹cm)


ارتفاع طبقه ۲.۹۰

باز می شود (جایگزین: ادغام = ۶.۹ m²)

سرویس از داخل حمام

واحد ۹۲.۰ = ۷۶.۲ m² بسته + ۱۵.۷ ایوان

هر

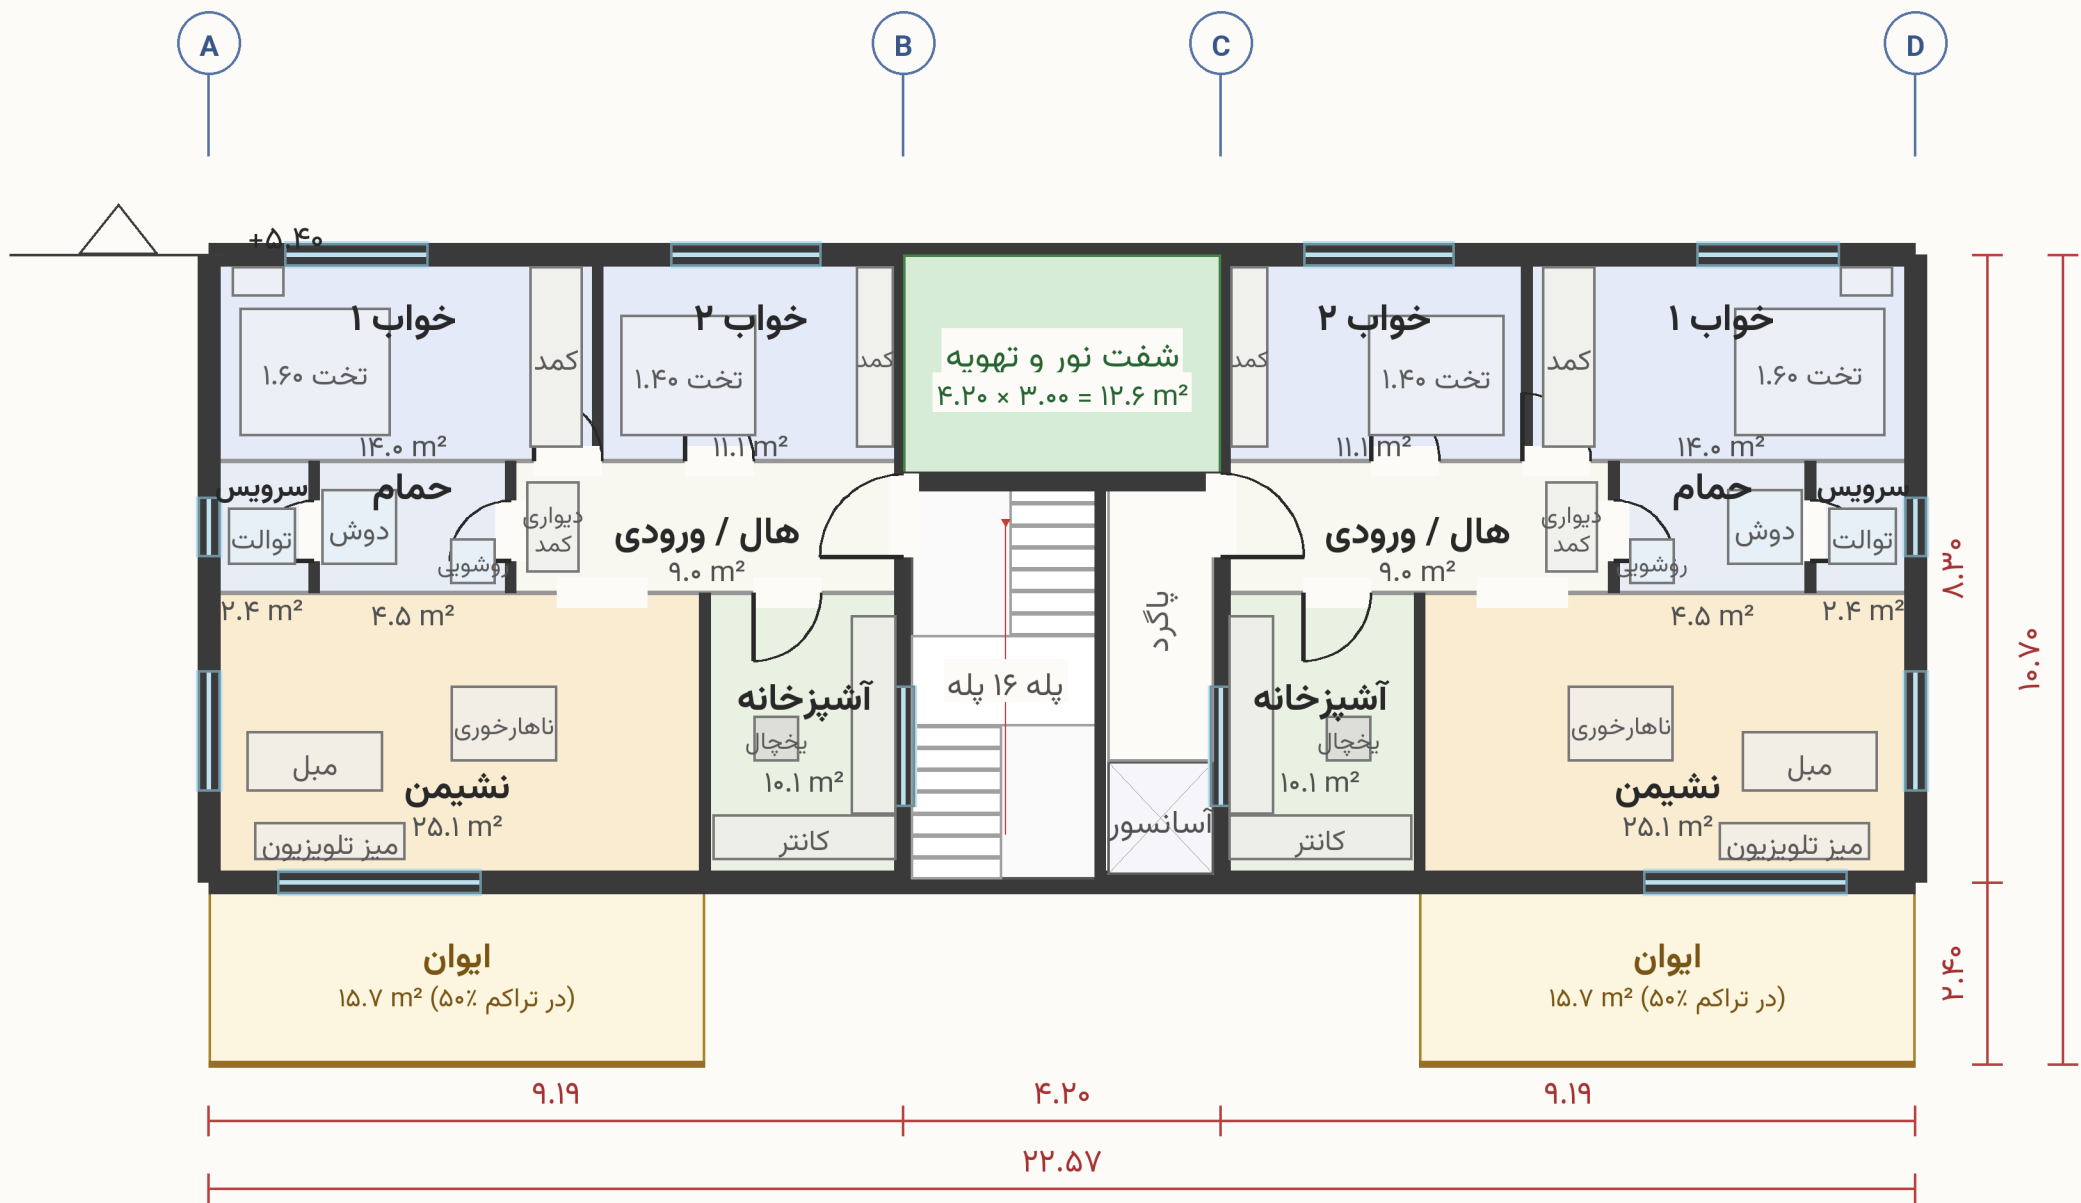

۵ متر

مقیاس ۱:۱۰۰

مجتمع مسکونی-تجاری

زمین ۵۴۲/۳۸ m² – اصفهان

عنوان نقشه

پلان بام

تراز

۱۹.۹۰+ متر

مقیاس

۱:۱۵۰

شماره برگه

A-۱۰۴

تاریخ

۱۴۰۵/۰۶/۲۷

ارتفاع کل

۲۰.۹ m

جدول فضاها

بام مسکونی
۱۸۷.۳
۲۲.۵۷×۸.۳۰

تراس پودیوم
۱۹۳
۱۸.۰۰×۱۰.۷۰


اتاقک پله/آسانسور
۲۱.۰
—

دهانه شفت
۱۲.۶
۴.۲۰×۳.۰۰

m (پودیوم ۵.۴۰ + ۲.۹۰×۵ + جان پناه ۱.۰۰)
ارتفاع تمام شده ۲۰.۹

آب با ارتفاع مفید زیر ۲.۲۰ معاف از تراکم
موتورخانه و منبع

ادامه باید و با کلاhek باران گیر پوشش شود
دهانه شفت تا بام

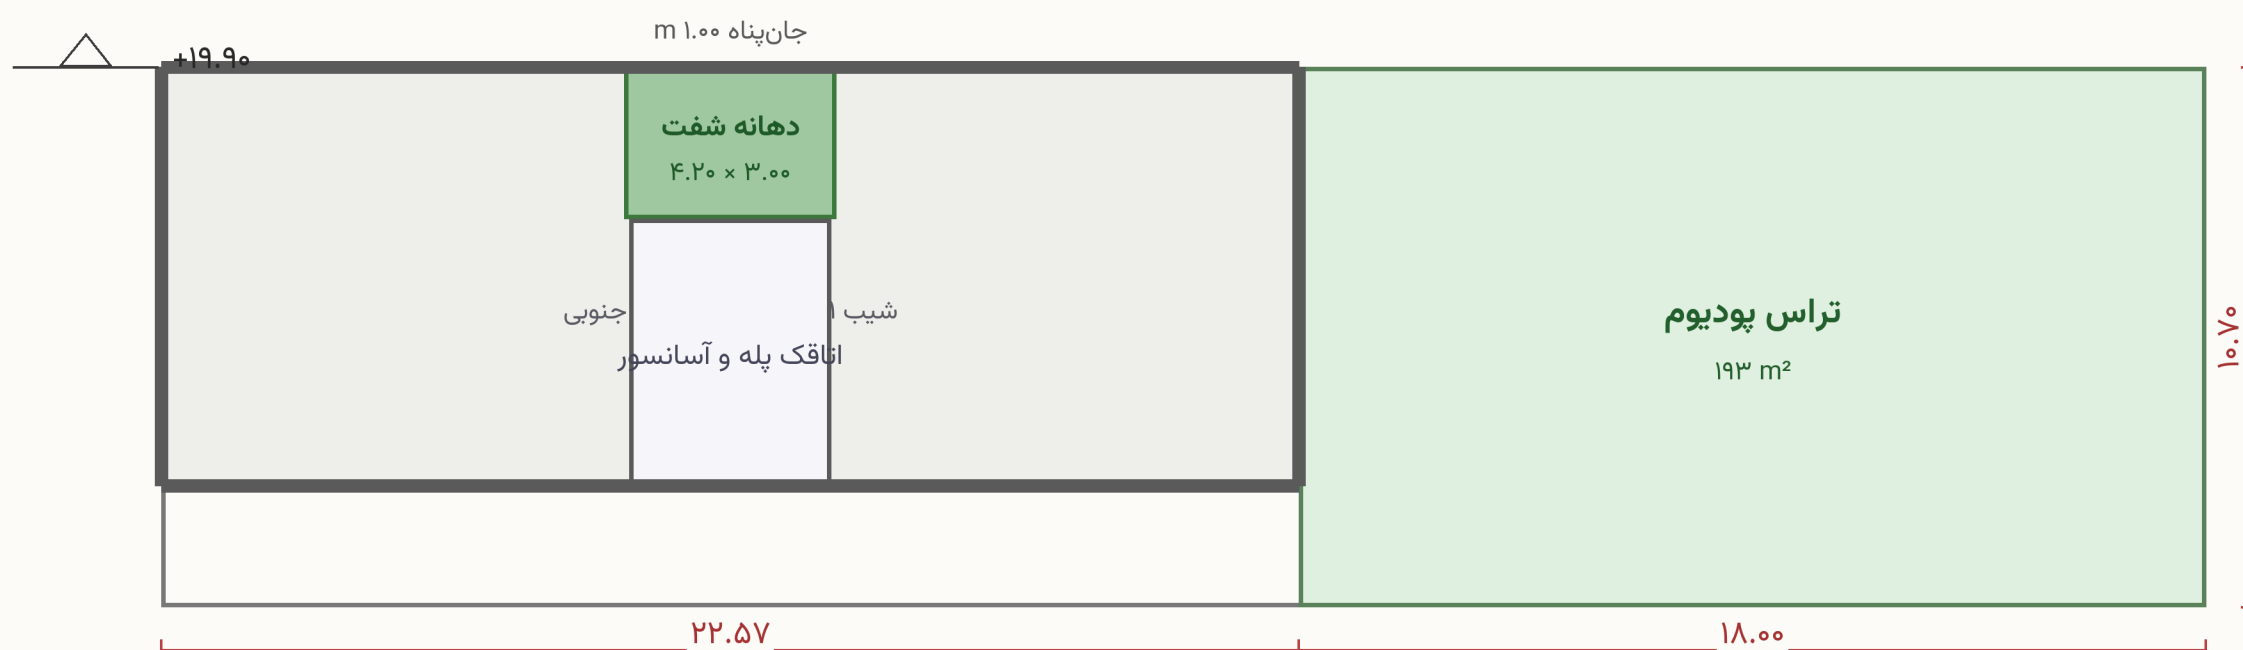

شمال

۵ متر

مقیاس ۱:۱۵۰