مجتمع مسکونی-تجاری

زمین ۵۴۲٫۳۸ m² — اصفهان

عنوان نقشه
پلان طبقه تیپ

تراز
+۵.۴۰ متر

مقیاس
۱:۱۰۰

شماره برگه
A-۱۰۳

تاریخ
۱۴۰۵/۰۶/۲۷

زیربنا
۱۹۰.۵ m²

جدول فضاها


نشیمن	۲۵.۱۲	۶.۵۶×۳.۸۳
آشپزخانه	۱۰.۰۶	۲.۶۳×۳.۸۳
سرویس	۲.۴۲	۱.۳۹×۱.۷۴
حمام	۴.۵۲	۲.۶۰×۱.۷۴
هال / ورودی	۹.۰۴	۵.۲۰×۱.۷۴
خواب ۱	۱۴.۰۳	۵.۱۴×۲.۷۳
خواب ۲	۱۱.۰۵	۴.۰۵×۲.۷۳
ایوان	۱۵.۷۰	۶.۵۶×۲.۴۰
پله/آسانسور/پاگرد	۲۲.۳۰	—
شفت نور و تهویه	۱۲.۶	۴.۲۰×۳.۰۰

· هسته و همسایگی ۲۵cm · تیغه ۱۵cm دیوار پیرامونی ۳۰cm

· پله رفت‌وبرگشتی ۱۶ پله (۲۹cm×۱۸.۱m) ارتفاع طبقه ۲.۹۰

باز می‌شود (جایگزین: ادغام = ۶.۹ m²) سرویس از داخل حمام

واحد ۹۲.۰ m² = ۷۶.۲ m² بسته + ۱۵.۷ ایوان هر

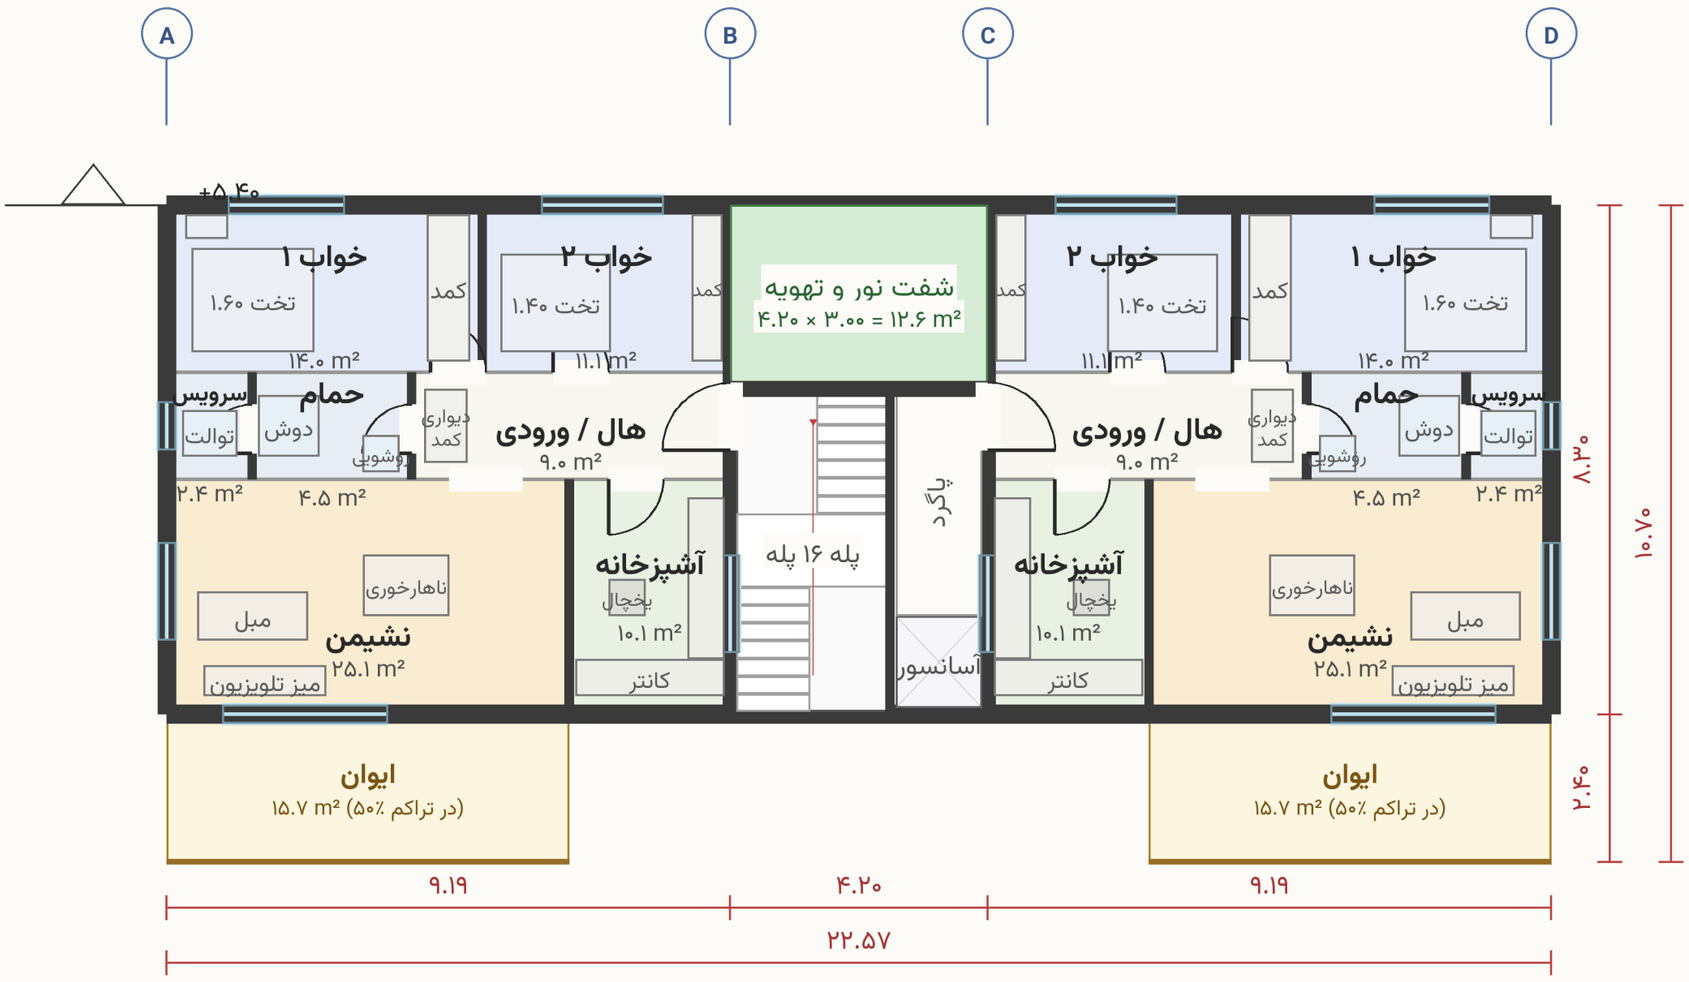

شمال

۰ ۵ متر

مقیاس ۱:۱۰۰