

زمین ۵۴۲/۳۸ m² - اصفهان

پلان همکف / پیلوت

±0.00 متر

1:150

A-101

1405/06/27

211.4 m²

۴۴.۹۰ مغازه ۱
۵.۹۹ × ۷.۵۰

۴۴.۹۰ مغازه ۲
۵.۹۹×۷.۵۰

۴۴.۹۰ مغازه ۳
۵.۹۹×۷.۵۰

انبار/سرویس


پارکینگ
۲.۵۰×۵.۰۰

۲۱.۴ لابی و هسته
۴.۲۰×۵.۱۰

ارتفاع مفید پیلوت ۲.۴۰ m معاف از تراکم
مغازه ۵.۴۰ m با نیم طبقه در، تا: ۲.۶۰ +

ارتفاع
واقعی یارکینگ ۱۲ تا ۱۴ فضا؛ اینجا ۶ فضا

نیاز
یا جریمه تبصره ۵ ماده ۱۰۰ جبران شود
کسری با زیرزمین

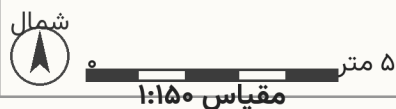

مجتمع مسکونی-تجاری

زمین ۵۴۲/۳۸ m² – اصفهان

عنوان نقشه

نیم طبقه و انباری

تراز

۲.۶۰+ متر

مقیاس

۱:۱۵۰

شماره برگه

A-۱۰۲

تاریخ

۱۴۰۵/۰۶/۲۷


زیربنا

انباری ۴۰ m²

جدول فضاها

۴۰.۰	انباری (۸ واحد) هرکدام ۵.۰ m ²
۲۷.۰	نیم طبقه ۱ ۵.۹۹×۴.۵۰
۲۷.۰	نیم طبقه ۲ ۵.۹۹×۴.۵۰
۲۷.۰	نیم طبقه ۳ ۵.۹۹×۴.۵۰

نیم طبقه تا ۵۵٪ مساحت مغازه مجاز است
تنها ۲۰٪ آن (۱۶.۲ m² از ۸۰.۹ m²) در تراکم
با ارتفاع مفید ۲.۲۰ m کاملاً معاف از تراکم
انباری
ارتفاع مفید نیم طبقه ۲.۵۰ m

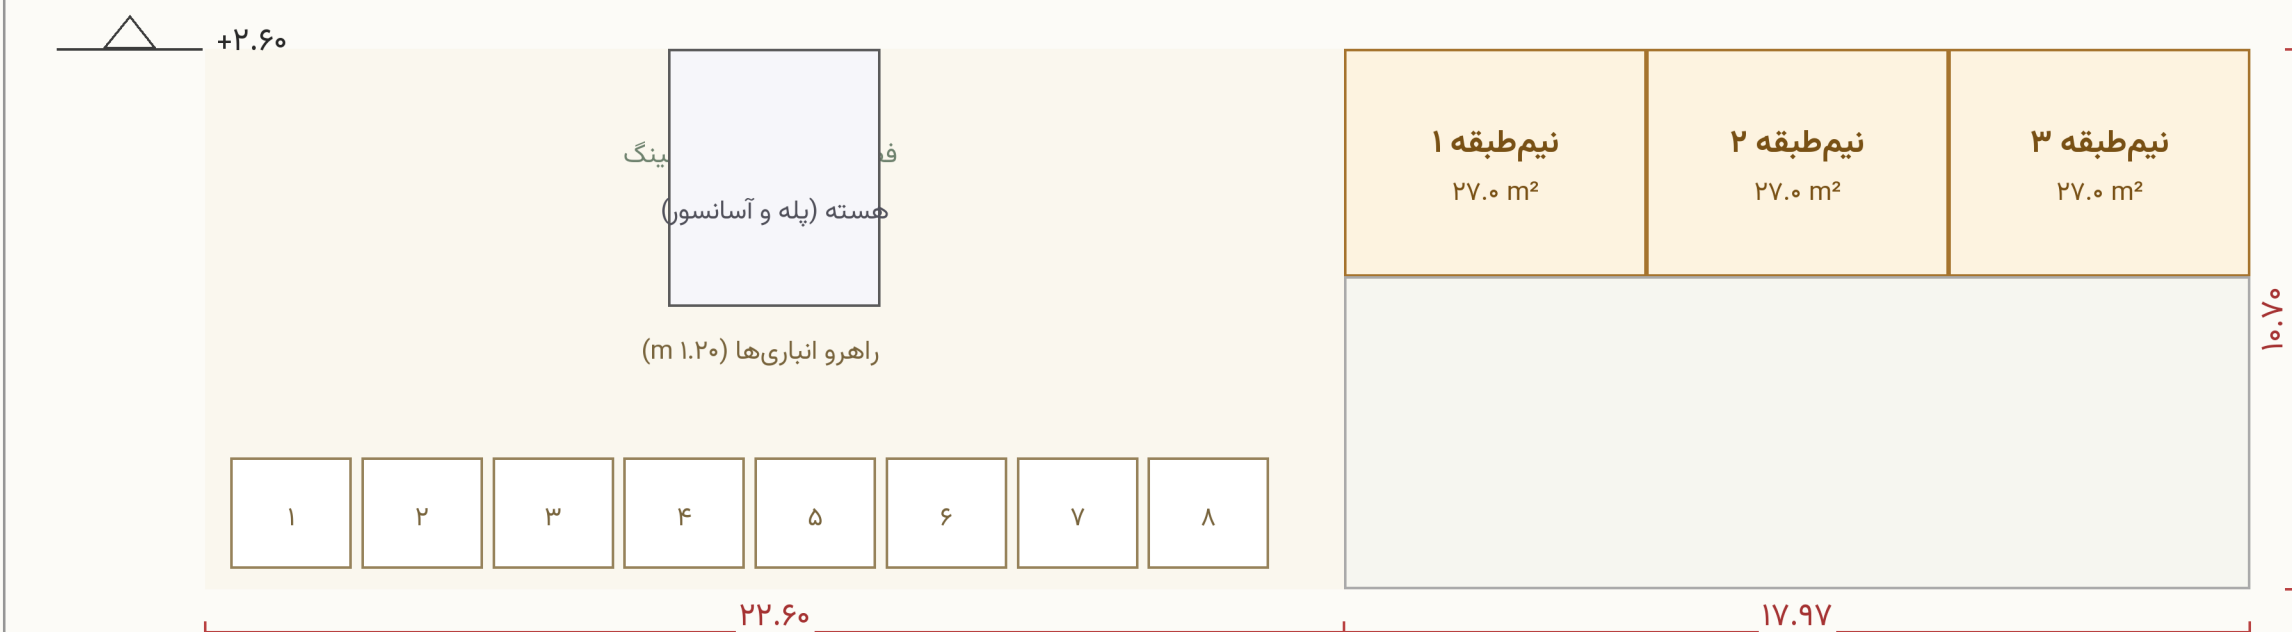

۵ متر

مقیاس ۱:۱۵۰

مجتمع مسکونی-تجاری

زمین ۵۴۲/۳۸ m² – اصفهان

عنوان نقشه

پلان طبقه تپ

تراز

۵.۴۰+ متر

مقیاس

۱:۱۰۰

شماره برگه

A-۱۰۳

تاریخ

۱۴۰۵/۰۶/۲۷

زیربنا

۱۹۰.۵ m²

جدول فضاها

نشیمین ۲۵.۱۲

۶.۵۶×۳.۸۳

آشپزخانه ۱۰.۰۶

۲.۶۳×۳.۸۳

سرویس ۲.۴۲

۱.۳۹×۱.۷۴

حمام ۴.۵۲

۲.۶۰×۱.۷۴

هال / ورودی ۹.۰۴

۵.۲۰×۱.۷۴

خواب ۱ ۱۴.۰۳

۵.۱۴×۲.۷۳

خواب ۲ ۱۱.۰۵

۴.۰۵×۲.۷۳

ایوان ۱۵.۷۰

۶.۵۶×۲.۴۰

پله/آسانسور/پاگرد ۲۲.۳۰

–

شفت نور و تهویه ۱۲.۶

۴.۲۰×۳.۰۰

· هسته و همسایگی ۲۵cm · تیغه ۱۵cm

دیوار پیرامونی ۳۰cm

· m · پله رفت و برگشتی ۱۶ پله (۱۸.۱×۲۹cm)


ارتفاع طبقه ۲.۹۰

باز می شود (جایگزین: ادغام = ۶.۹ m²)

سرویس از داخل حمام

واحد ۹۲.۰ = ۷۶.۲ m² = بسته + ۱۵.۷ ایوان

هر

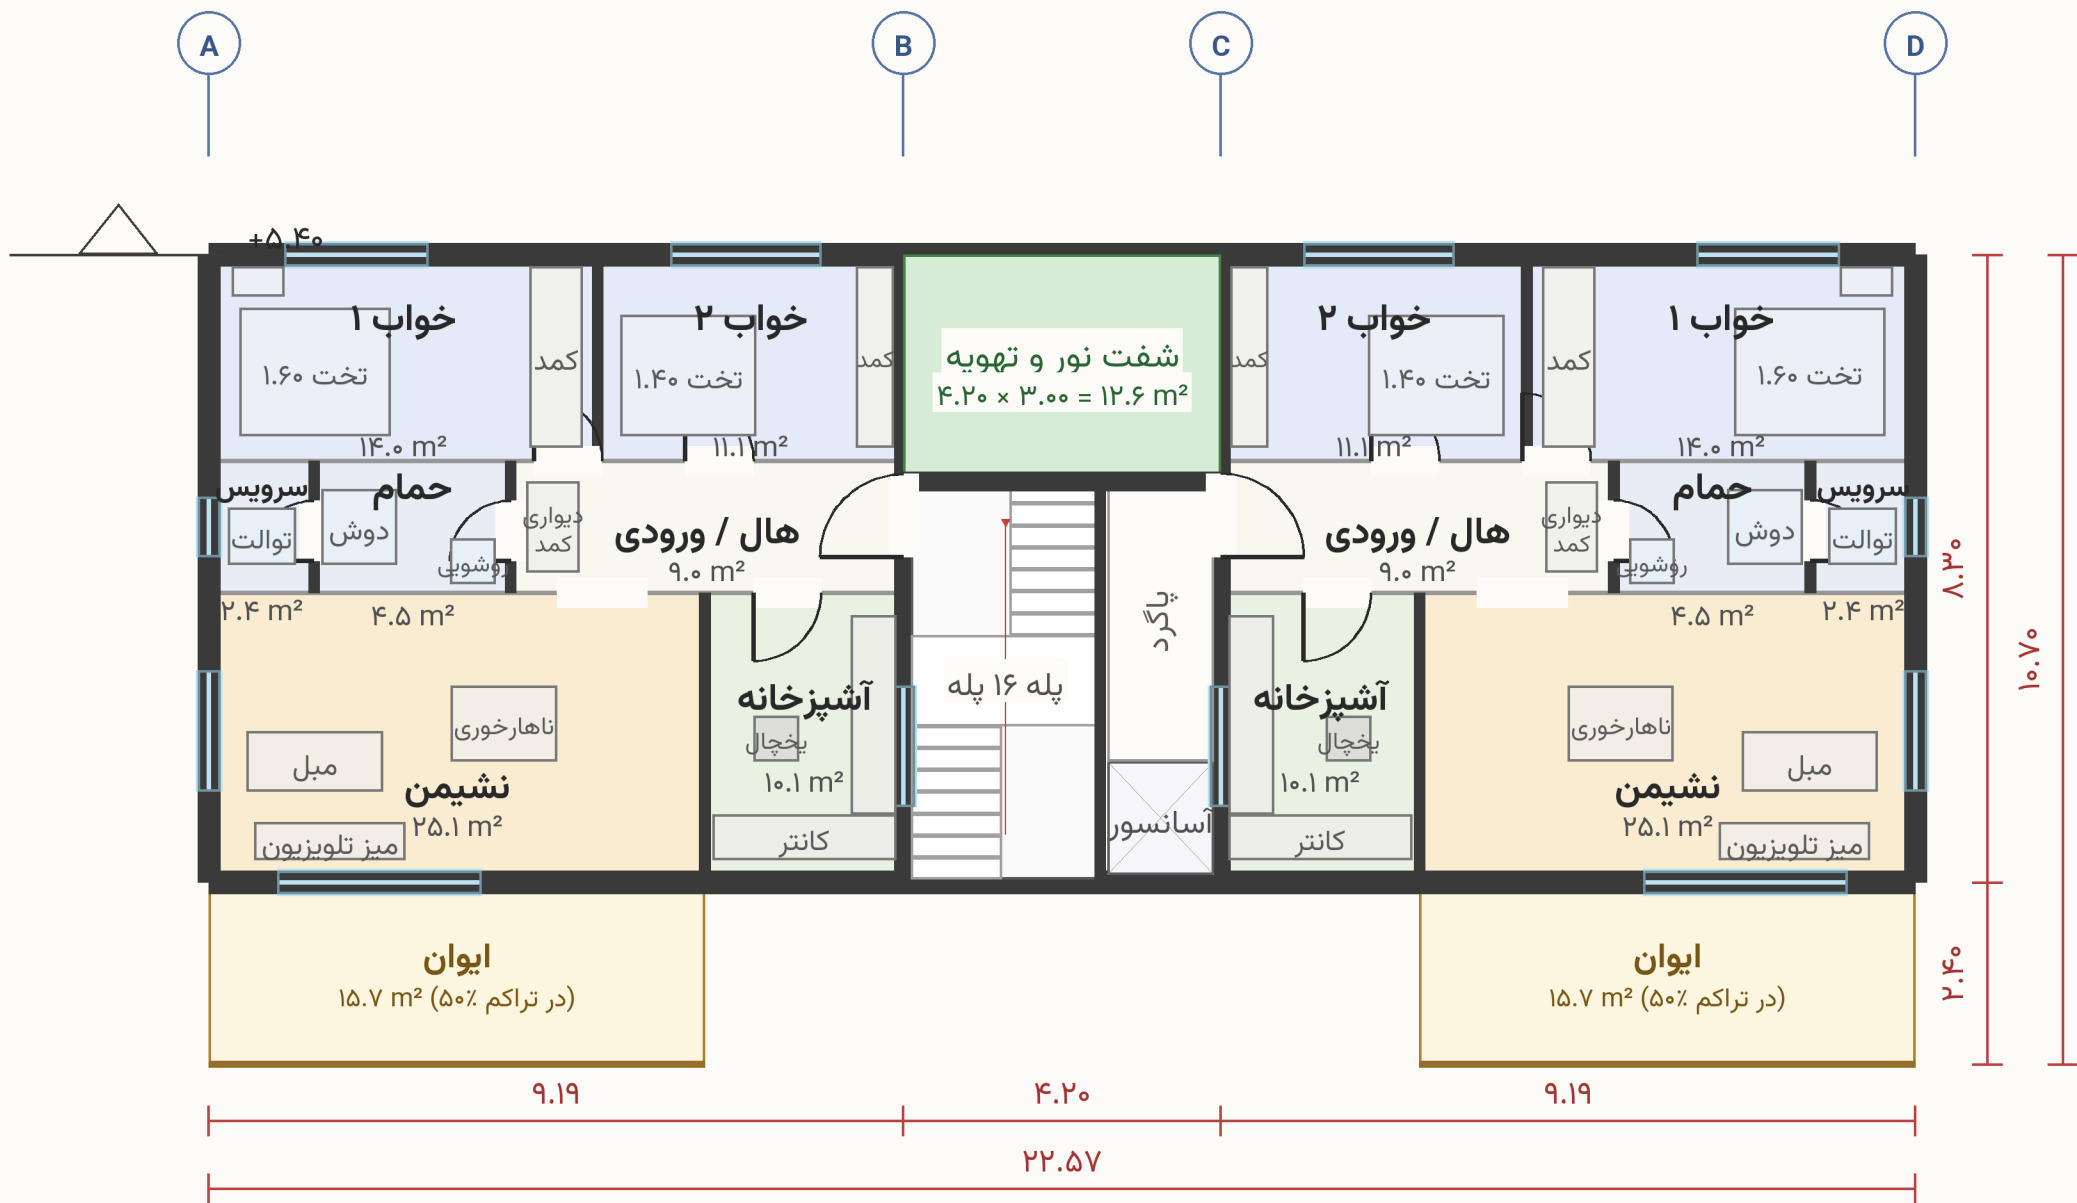

مقیاس ۱:۱۰۰

مجتمع مسکونی-تجاری

زمین ۵۴۲/۳۸ m² – اصفهان

عنوان نقشه

پلان بام

تراز

۱۹.۹۰+ متر

مقیاس

۱:۱۵۰

شماره برگه

A-۱۰۴

تاریخ

۱۴۰۵/۰۶/۲۷

ارتفاع کل

۲۰.۹ m

جدول فضاها

بام مسکونی
۱۸۷.۳
۲۲.۵۷×۸.۳۰

تراس پودیوم
۱۹۳
۱۸.۰۰×۱۰.۷۰


اتاقک پله/آسانسور
۲۱.۰
—

دهانه شفت
۱۲.۶
۴.۲۰×۳.۰۰

m (پودیوم ۵.۴۰ + ۲.۹۰×۵ + جان پناه ۱.۰۰)
ارتفاع تمام شده ۲۰.۹

آب با ارتفاع مفید زیر ۲.۲۰ معاف از تراکم
موتورخانه و منبع

ادامه باید و با کلاhek باران گیر پوشش شود
دهانه شفت تا بام

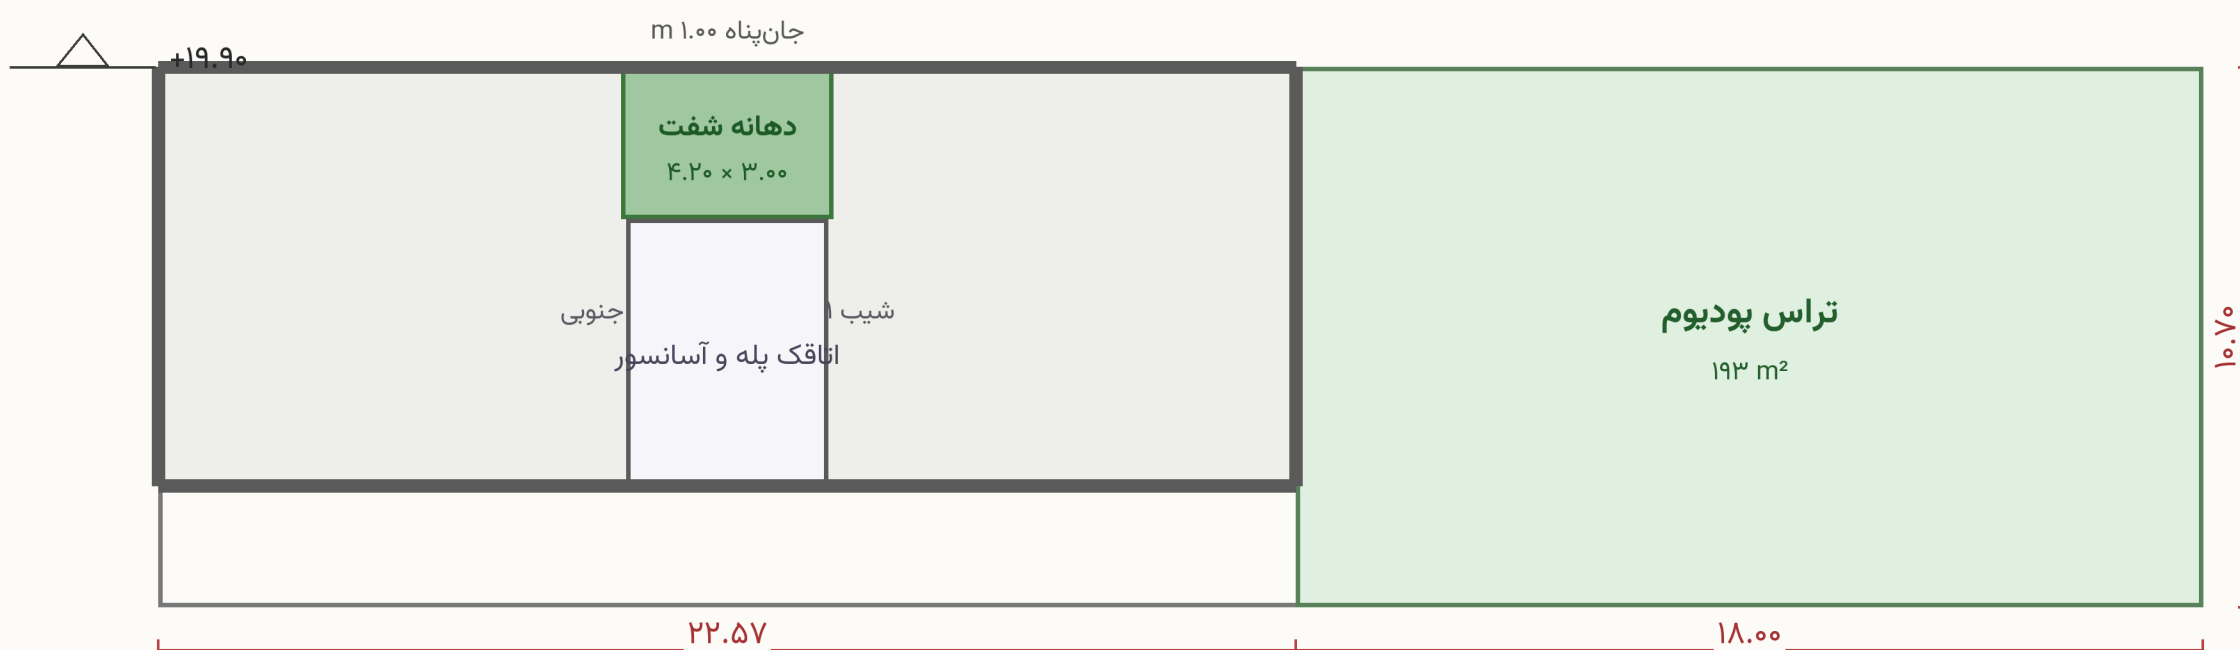

شمال

۵ متر

مقیاس ۱:۱۵۰